



Žemės sklypo išdėstymo schema

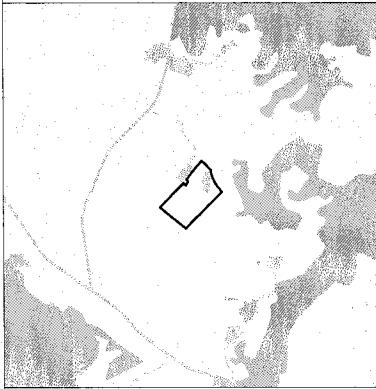

# ŽEMĖS SKLYPO PLANAS M 1:1000

Sklypo plotas 26838 m<sup>2</sup>

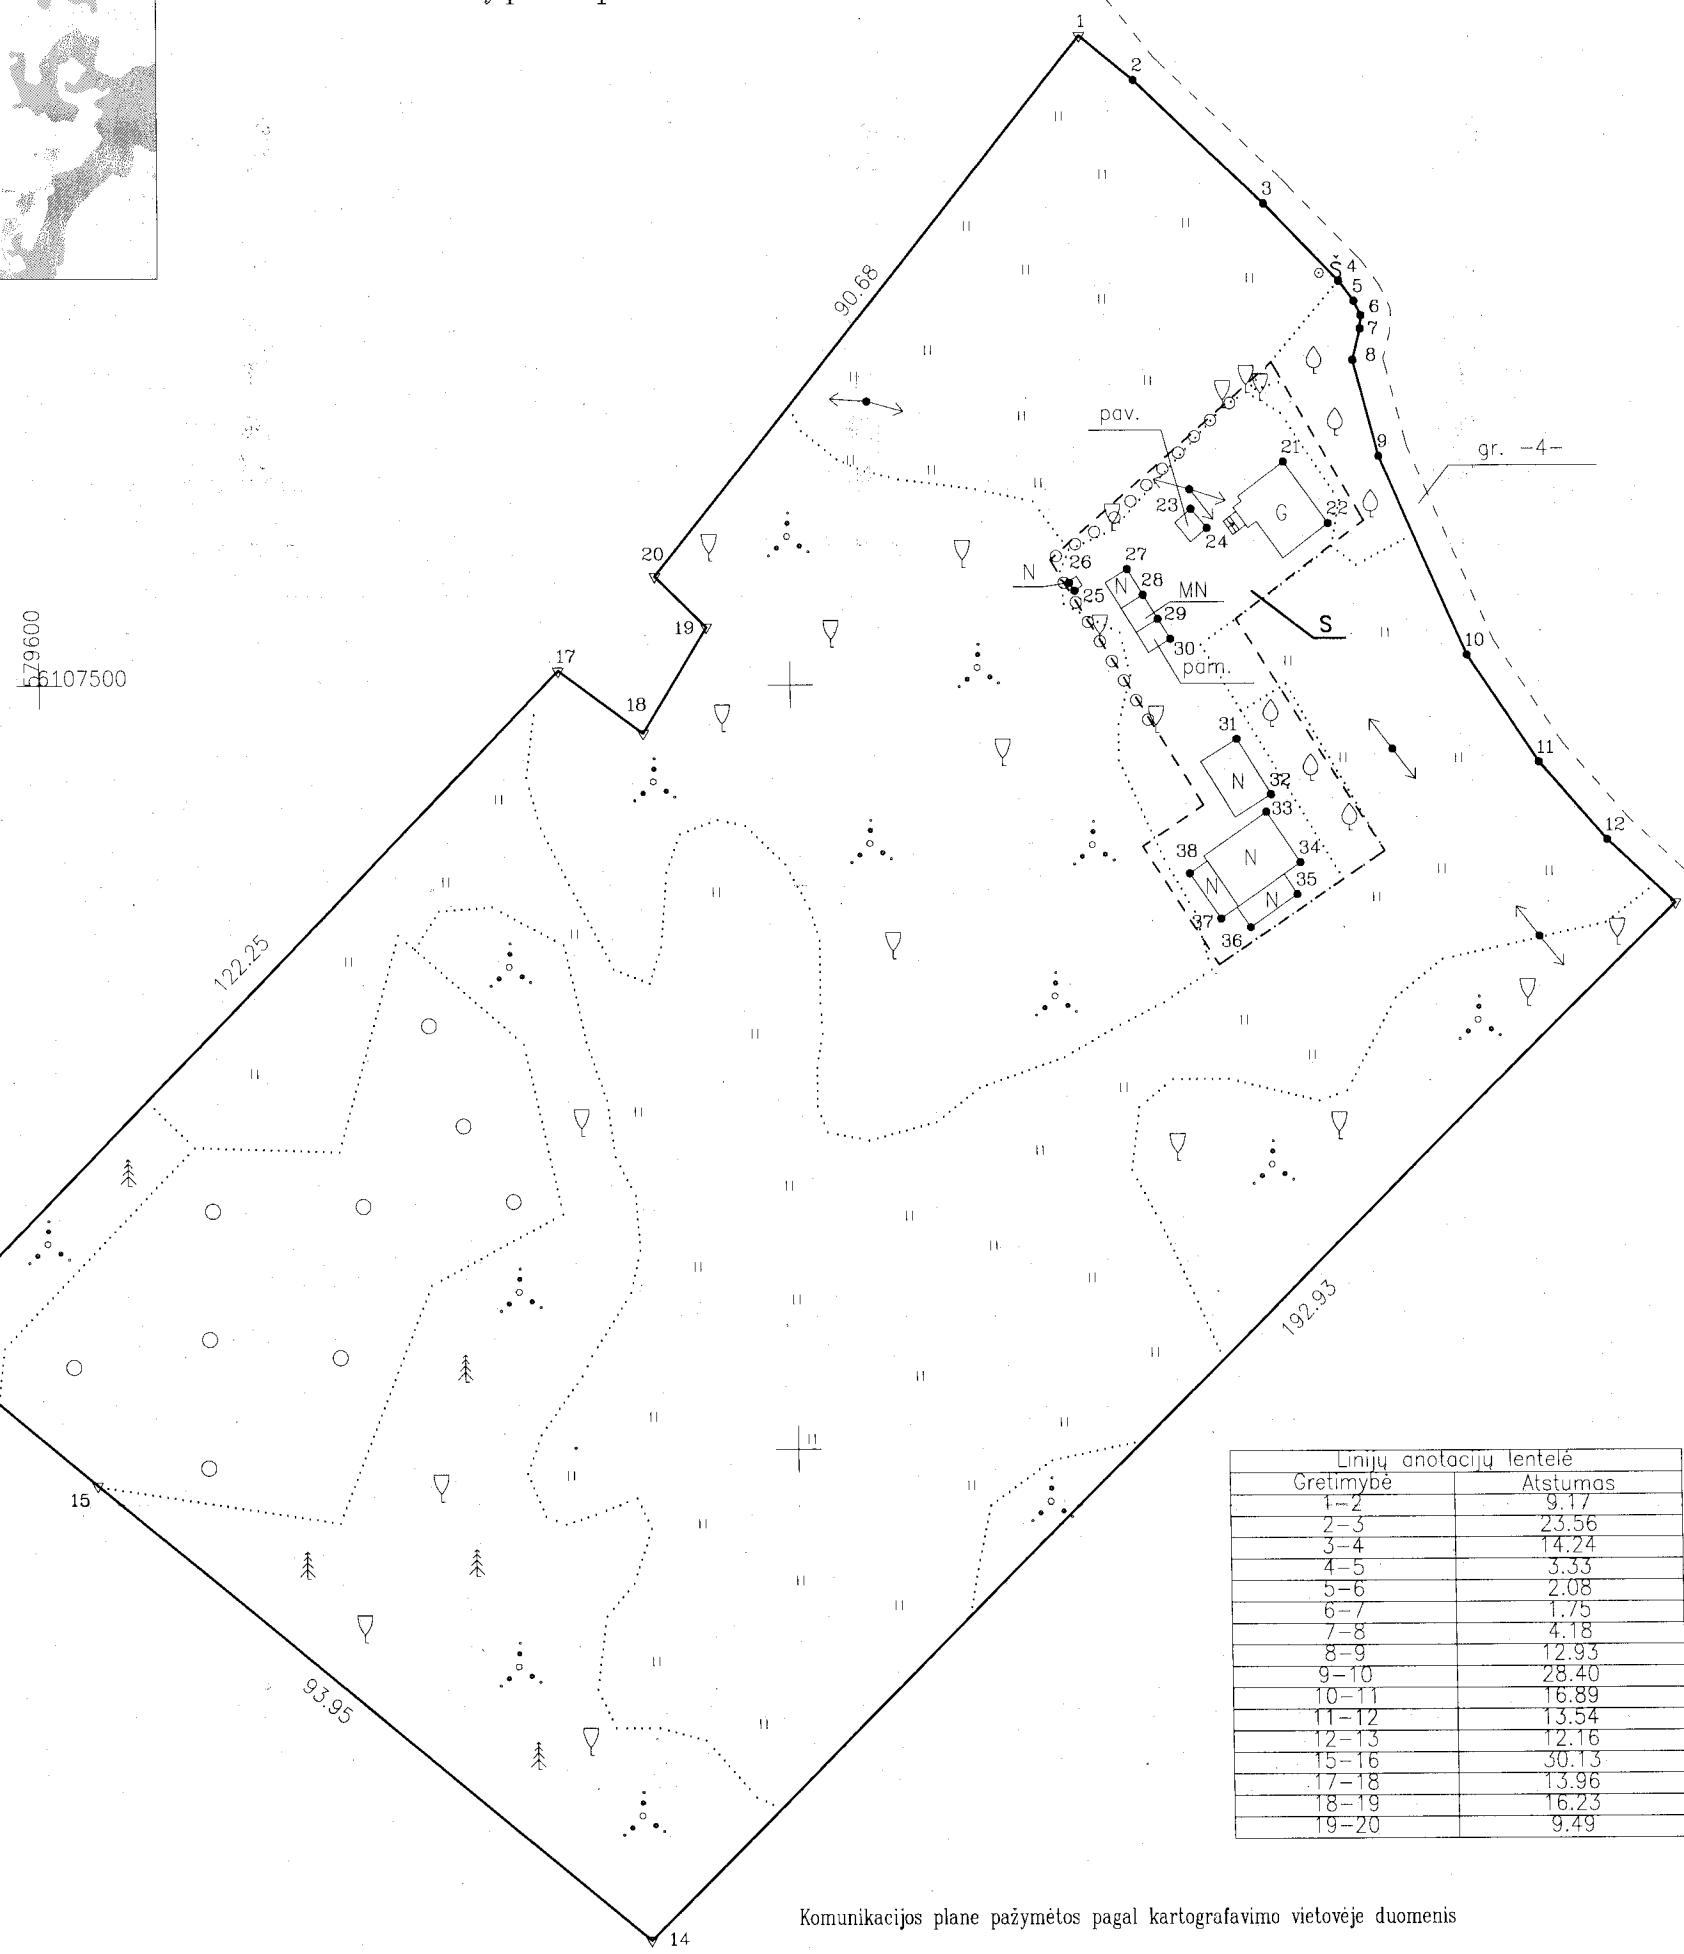

Kadastro:	vietovė	Dūdėnų	blokas	sklypas
Žemės sklypo kadastro Nr.	6 2 2 4 0 0 0 4			

Savivaldybė	Molėtų r.
Seniūnija	Giedraičių
Gyvenamoji vietovė	Bekupės k.
Gatvė, namo Nr.	Vingio g. 3

Gretimybė	Gretimo žemės sklypo kadastro Nr.	Pastabos
1-13		4m kelias
13-14	6224/0004:0120	
14-15	6224/0004:0168	
15-16	6224/0004:0179	
16-1	6224/0004:0203	atlirk kadastriniai matavimai

Su pagal 2025-06-05 atlirką žemės sklypo ribų paženklinimą-parodyma,  
parengtame žemės sklypo plane išbraižytomis ribomis ir apskaičiuotu žemės sklypo plotu sutinku:

JADVYGA MICKEVICIENĖ (igal. Darius Juodis)

(žemės sklypo savininko (esamojo arba būsimojo) vardas, pavardė)

2025-06-05  
(data)

## UAB "Žemės matavimų grupė"

Įm. k. 301791912, matininko kvalifikacijos Nr. 2M-M-369  
tel. +37064500772, matavimugrupe@gmail.com  
Sodžiaus g. 9, Širvintos arba Laisvės pr. 60-1016, Vilnius

Pareigos matininkas	Parašas	Vardas, pavardė	Data
		Vitalijus Jariomenko	2025-06-05

