
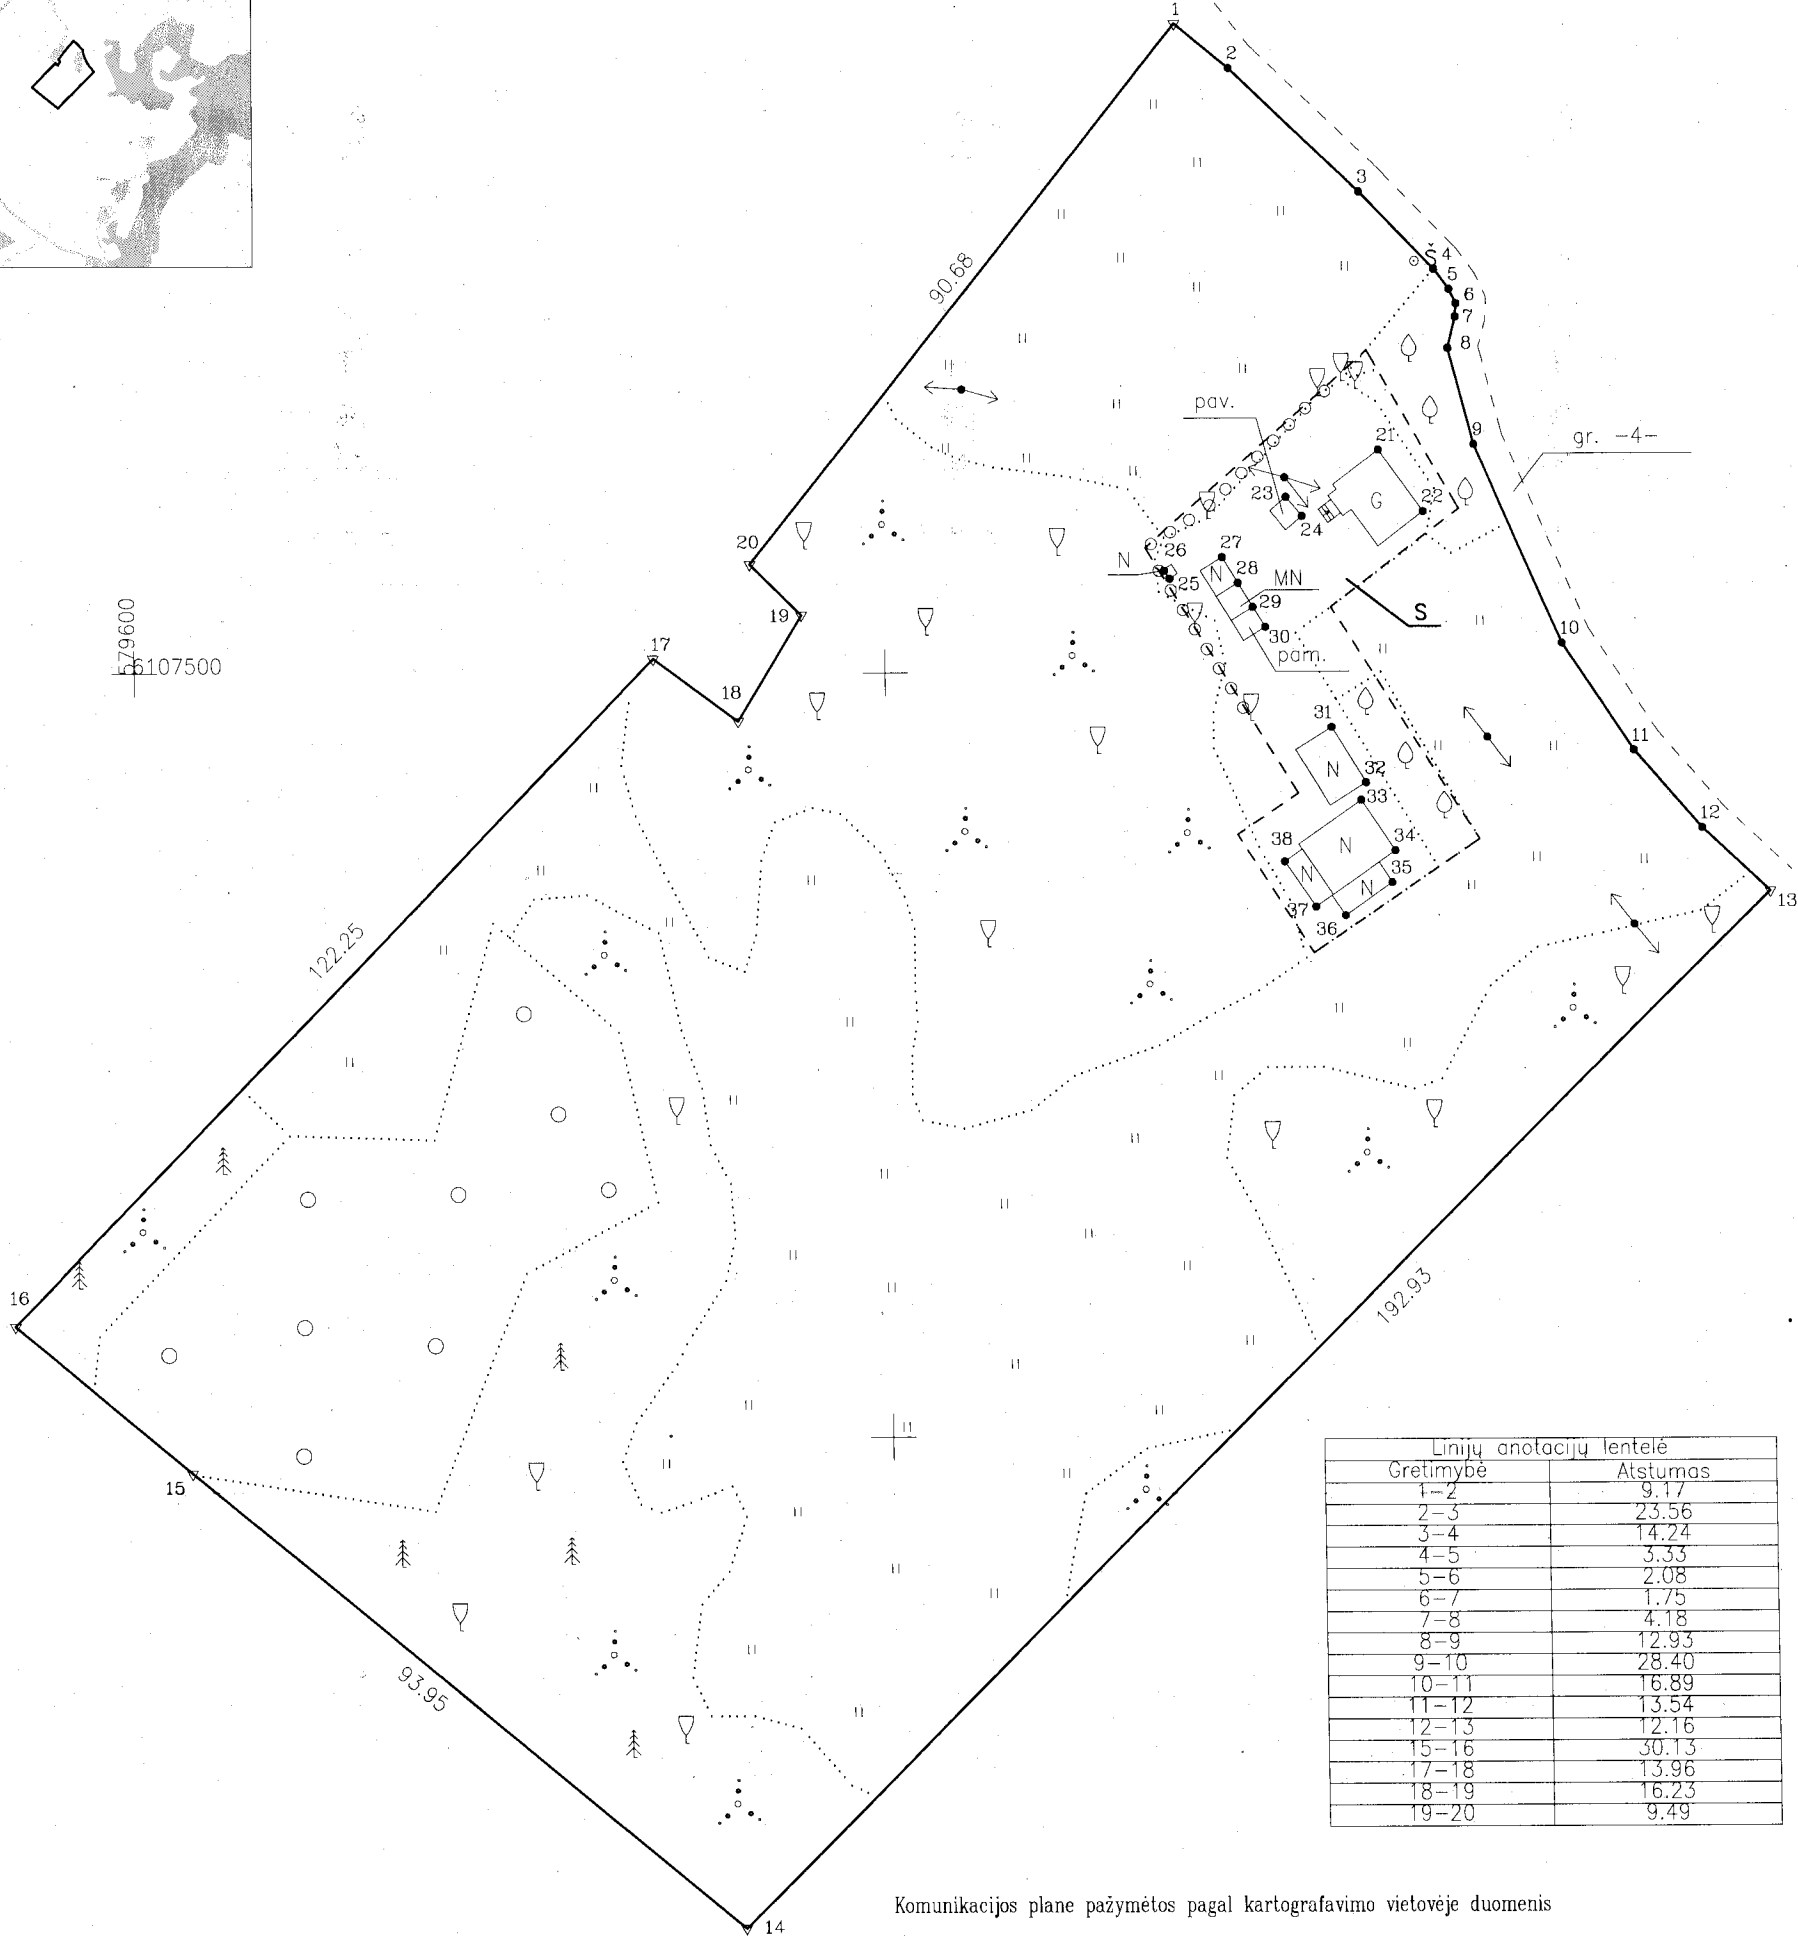


ŽEMĖS SKLYPO PLANAS M 1:1000

Sklypo plotas 26838 m²

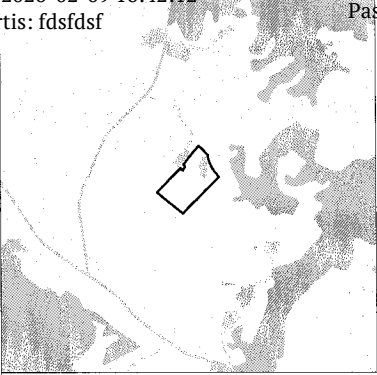

Linijų anotacijų lentelė	
Gretimybė	Atstumas
1-2	9.17
2-3	23.56
3-4	14.24
4-5	3.33
5-6	2.08
6-7	1.75
7-8	4.18
8-9	12.93
9-10	28.40
10-11	16.89
11-12	13.54
12-13	12.16
15-16	30.13
17-18	13.96
18-19	16.23
19-20	9.49

Komunikacijos plane pažymėtos pagal kartografavimo vietovėje duomenis

Kadastro:	vietovė	Dudėnų					Dokumentą elektroniniu parašu pasirašė ROBERTAS MIŠKINIS	
Žemės sklypo kadastro Nr:							6	2
							2	4
							0	0

Savivaldybė	Molėtų r.
Seniūnija	Giedraičių
Gyvenamoji vietovė	Bekupės k.
Gatvė, namo Nr.	Vingio g. 3

Gretimybė	Gretimo žemės sklypo kadastro Nr.	Pastabos
1-13		4m kelias
13-14	6224/0004:0120	
14-15	6224/0004:0168	
15-16	6224/0004:0179	
16-1	6224/0004:0203	atlikti kadastriniai matavimai

Su pagal 2025-06-05 atliktą žemės sklypo ribų pažėklinimą-parodymą,
parengtame žemės sklypo plane išbraižytais ribomis ir apskaičiuotu žemės sklypo plotu sutinku.

JADVGA MICKEVIČIENE (igal. Darius Juodis)
(žemės sklypo savininko (esamojo arba būsimojo) vardas, pavardė)

(parašas)

2025-06-05
(data)

UAB "Žemės matavimų grupė"

im.k. 301791912, matininko kvalifikacijos Nr. 2M-M-369
tel. +37064500772, matavimugrupe@gmail.com
Sodžiaus g. 9, Sirvintos arba Laisvės pr. 60-1016, Vilnius

Pareigos	Parašas	Vardas, pavardė	Data
matininkas		Vitalijus Jariomenko	2025-06-06

Dokumentą elektroniniu parašu
pasirašė ROBERTAS MIŠKINIS
Data: 2026-02-09 16:35:48
Paskirtis: fdfsfd

